
CLUB PER STUDENTI


CLUB FOR STUDENT

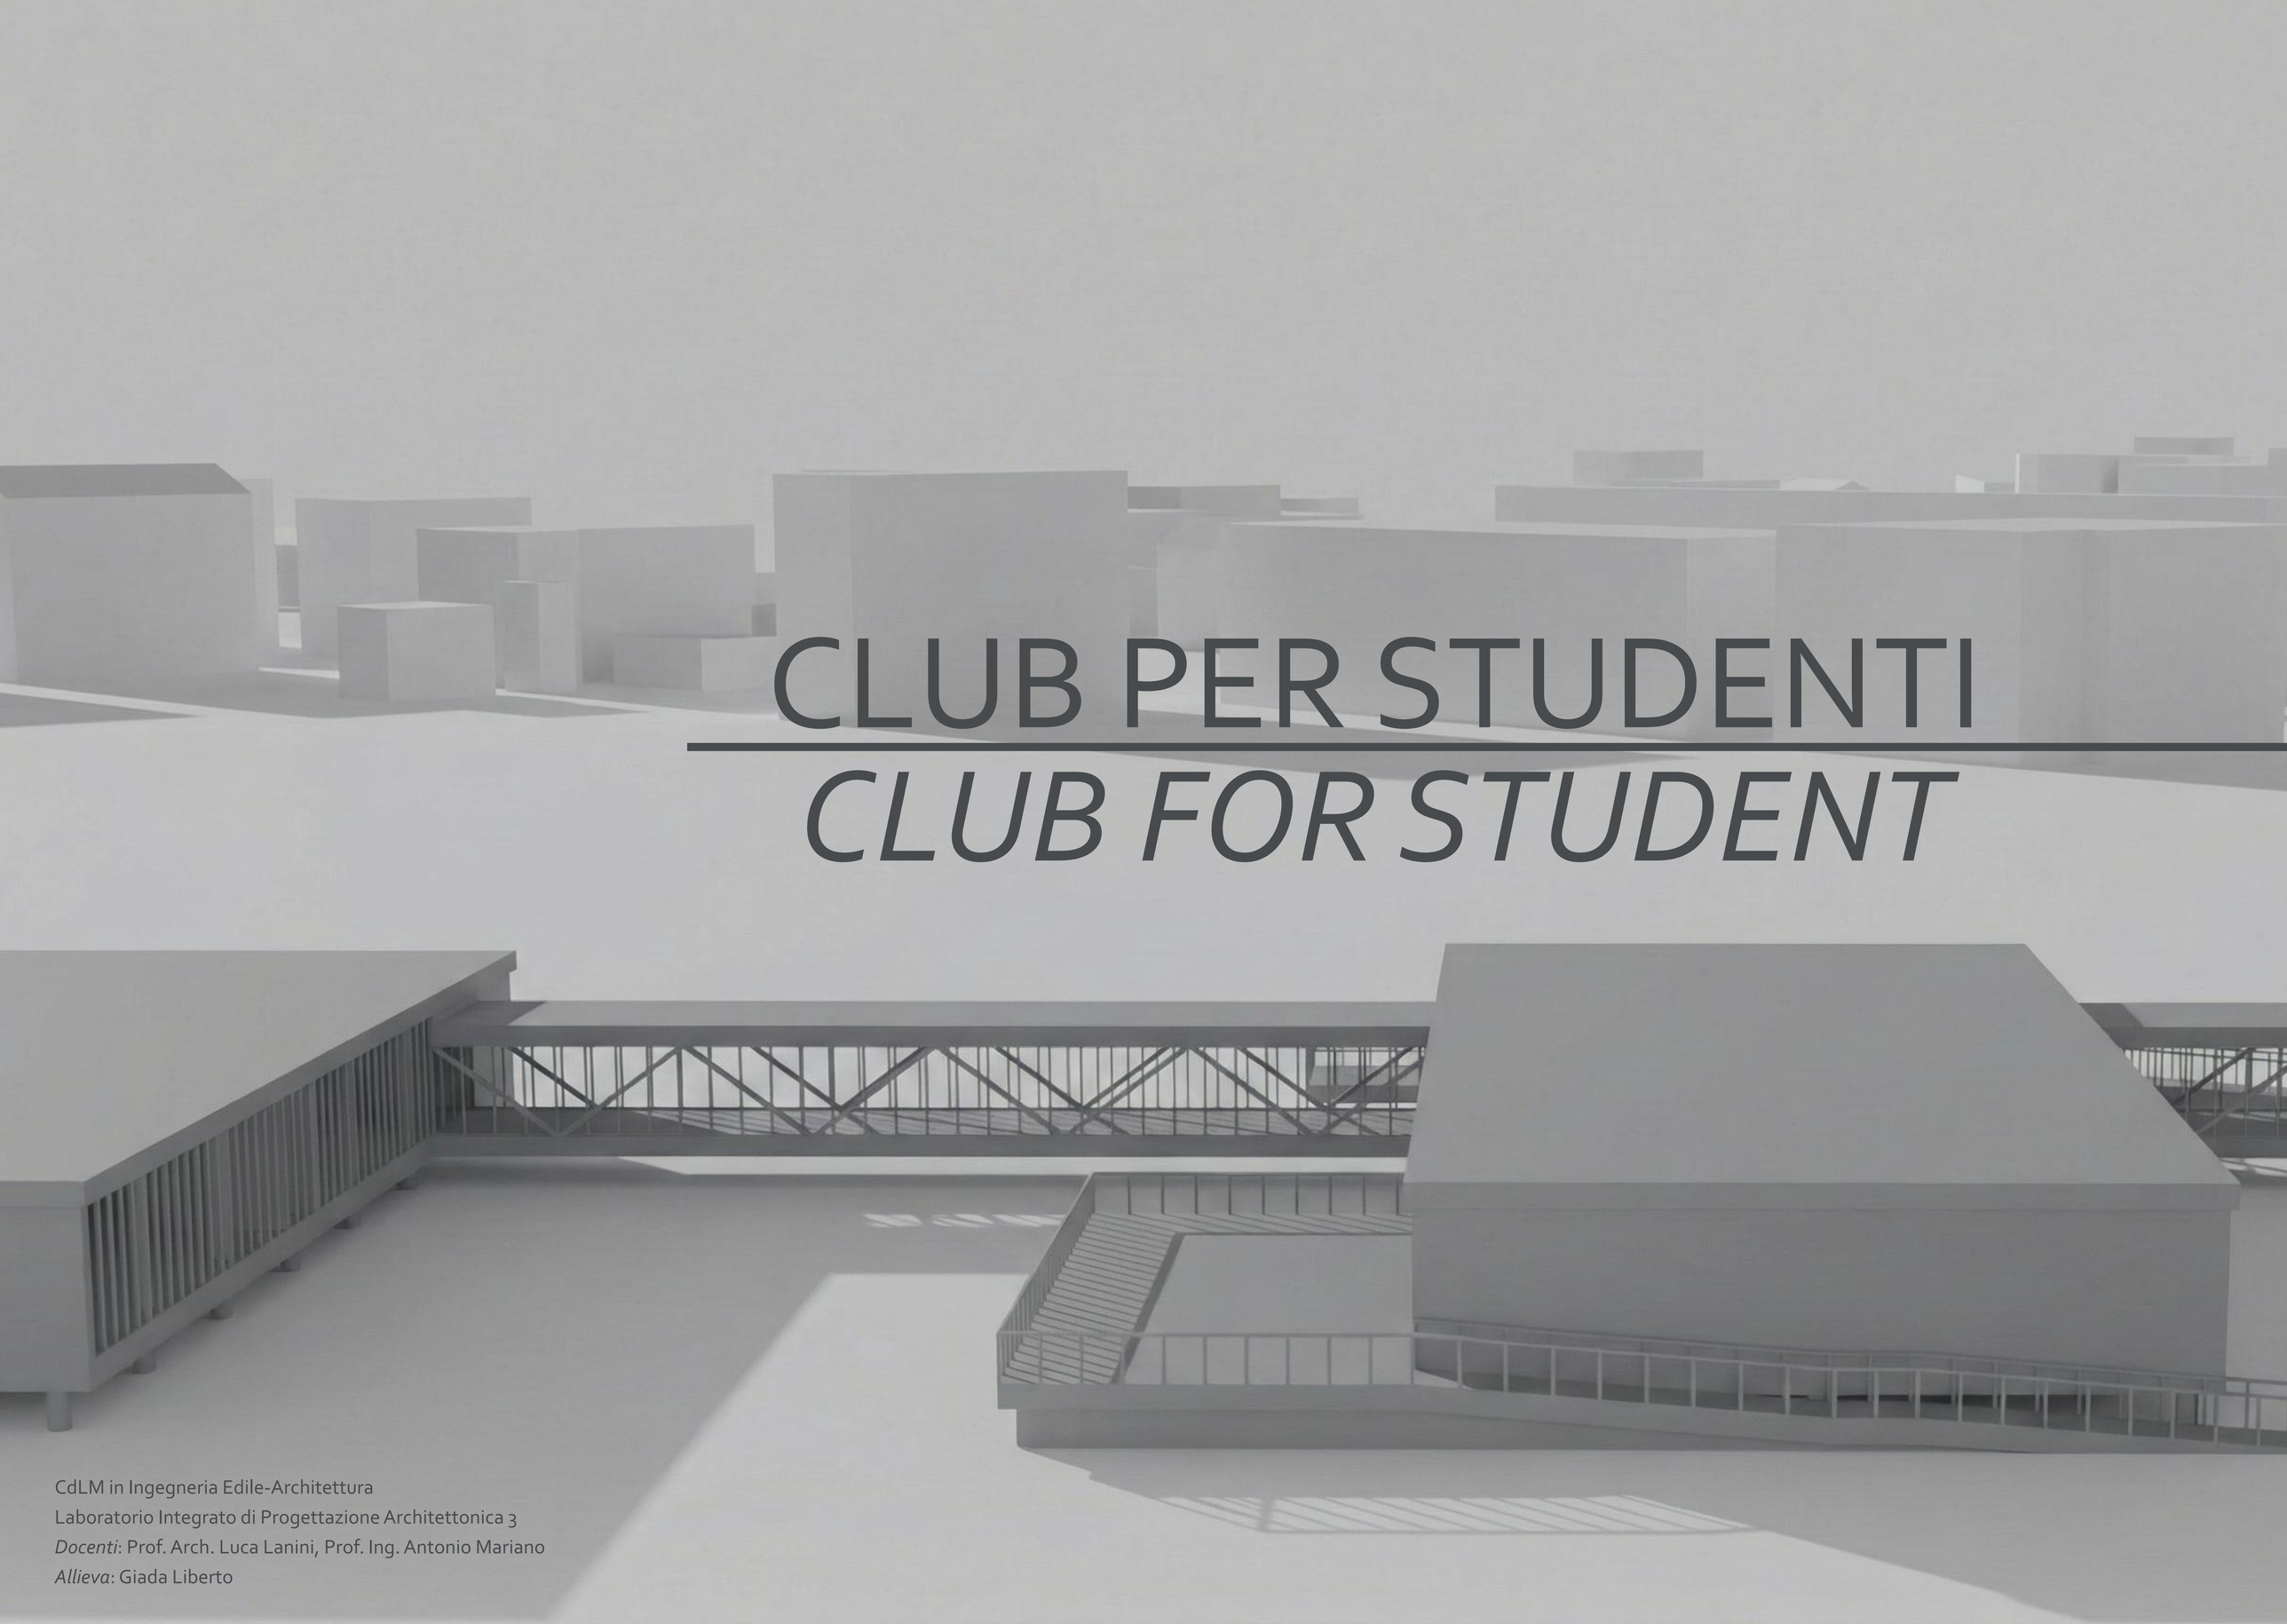

CdLM in Ingegneria Edile-Architettura
Laboratorio Integrato di Progettazione Architettonica 3
Docenti: Prof. Arch. Luca Lanini, Prof. Ing. Antonio Mariano
Allieva: Giada Liberto

CONTESTO URBANO

URBAN CONTEXT

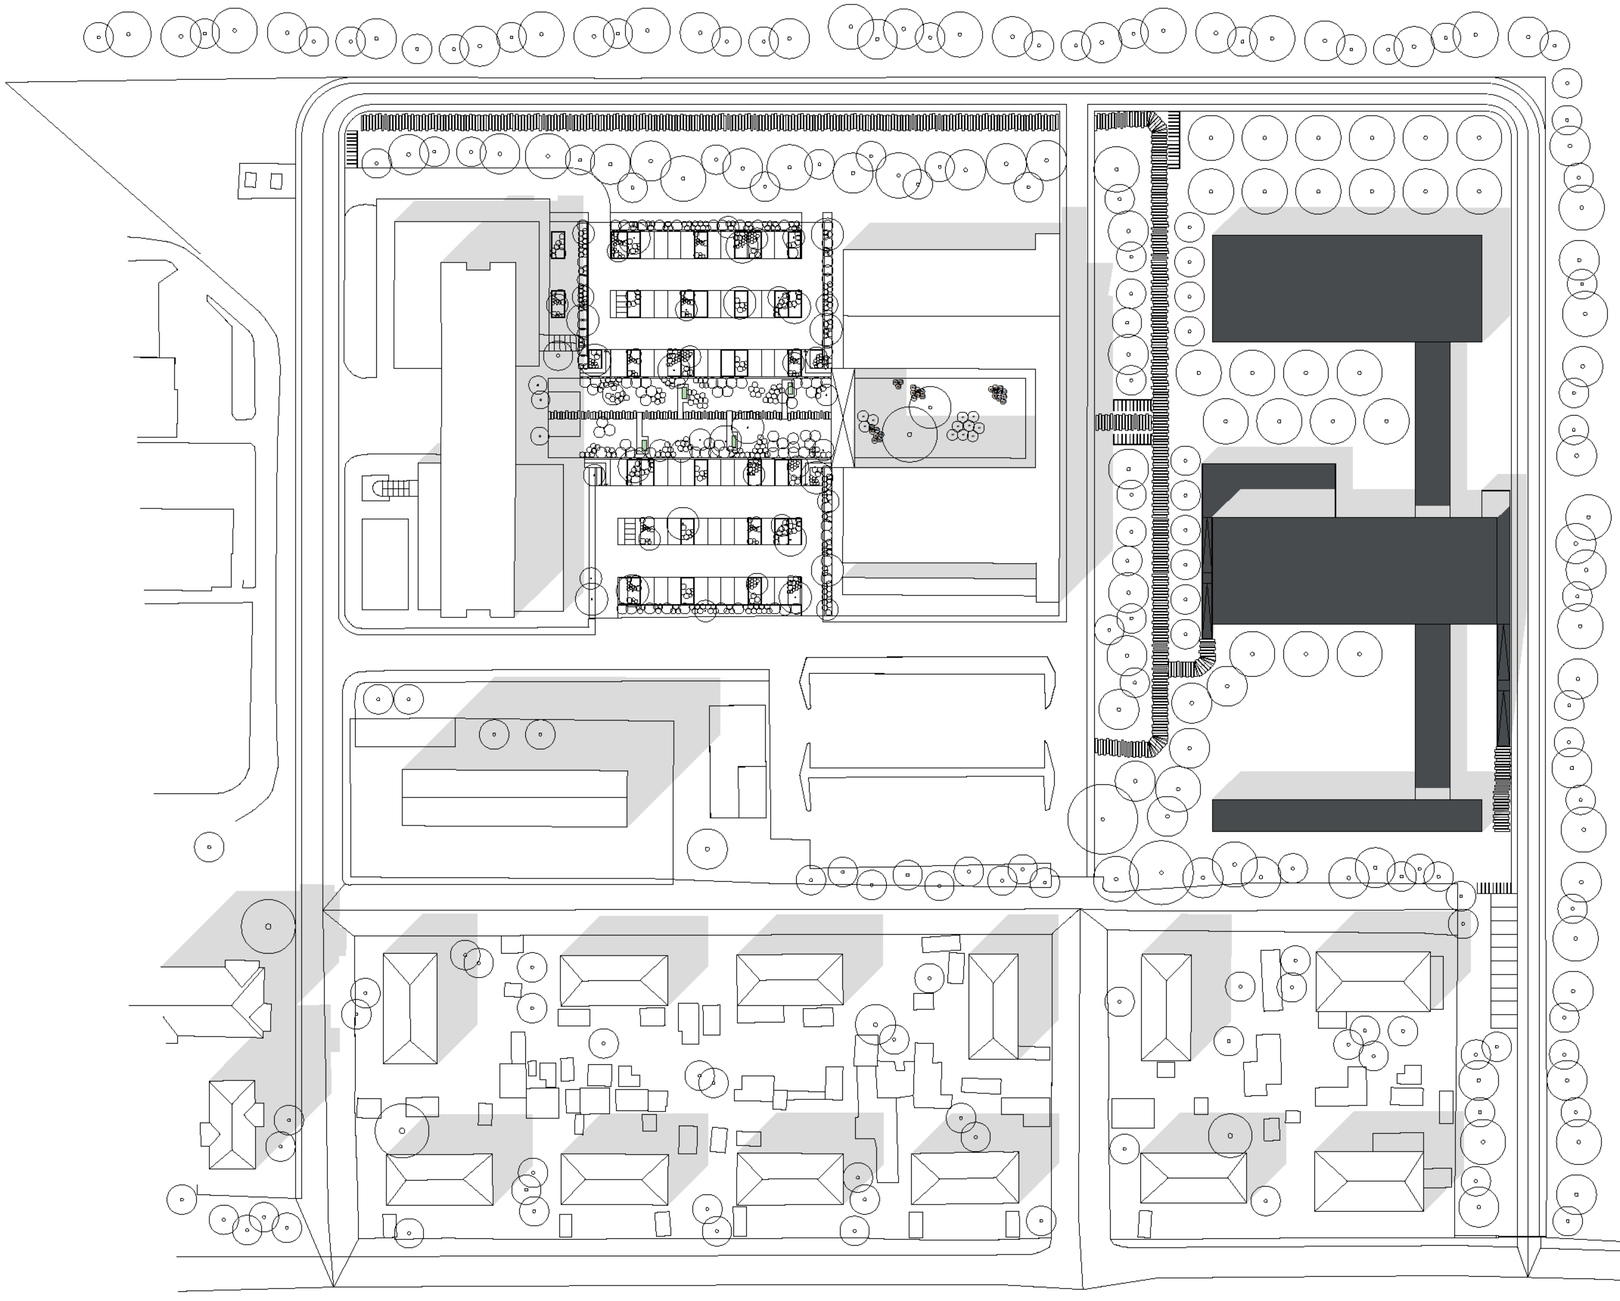

Planimetria - *Plan*
Scala 1:400 - *Scale 1:400*


Il progetto descrive il concetto architettonico e funzionale per la realizzazione di un nuovo Club per Studenti, ponendo l'accento sul dialogo con il contesto archeologico e sulla chiarezza distributiva degli spazi. Il progetto si sviluppa come un organismo architettonico concepito per dialogare in modo dinamico con il contesto storico e archeologico circostante, in particolare le necropoli presenti nell'area. La sua configurazione planimetrica, a pettine, risponde all'esigenza di valorizzare e inquadrare visivamente le preesistenze, creando una sequenza di corti e affacci che ne permettono la percezione. L'accesso al lotto è garantito da tre ingressi distinti. L'ingresso principale è collocato in basso a destra ed è collegato alla rampa d'accesso principale, poi vi è l'ingresso di continuità che è posizionato centralmente, ed è progettato per raccordarsi armonicamente con l'esistente confinante e infine si ha un ingresso situato in basso a sinistra, a servizio delle aree esterne.

This document describes the architectural and functional concept for the realization of a new Student Club, focusing on the dialogue with the archaeological context and the clarity of spatial distribution. The project develops as an architectural organism conceived to dynamically engage with the surrounding historical and archaeological context, particularly the necropolises present in the area. Its comb-like planimetric configuration is designed to enhance and visually frame the existing structures, creating a sequence of courtyards and views that allow for their perception. Access to the lot is provided by three distinct entrances. The main entrance is located at the bottom right and is connected to the principal access ramp; then there is the continuity entrance, centrally positioned and designed to harmonically connect with the existing adjacent structure; finally, there is an entrance located at the bottom left, serving the external areas.

FORME ARCHITETTONICHE

ARCHITECTURAL FORMS

La struttura è composta da tre blocchi principali paralleli, interconnessi da due elementi volumetrici secondari che fungono da strutture a ponte e sale espositive. Il primo blocco è il volume più a valle, con larghezza di 6 metri; mentre il secondo blocco, quello centrale, e il terzo blocco, quello superiore, sono caratterizzati da una maggiore ampiezza, pari a 20 metri. La percezione esterna dei blocchi è volutamente opaca e monolitica, conferendo all'edificio l'aspetto di un blocco unico e introverso, quasi "staccato" dal contesto. In netta contrapposizione, le facciate interne e le pareti che si affacciano tra i blocchi che sono caratterizzate da ampie vetrate continue. Questo espediente formale garantisce massima illuminazione naturale e permette affacci visivi tra le diverse ali della struttura, enfatizzando la funzione di sala espositiva delle strutture a ponte.

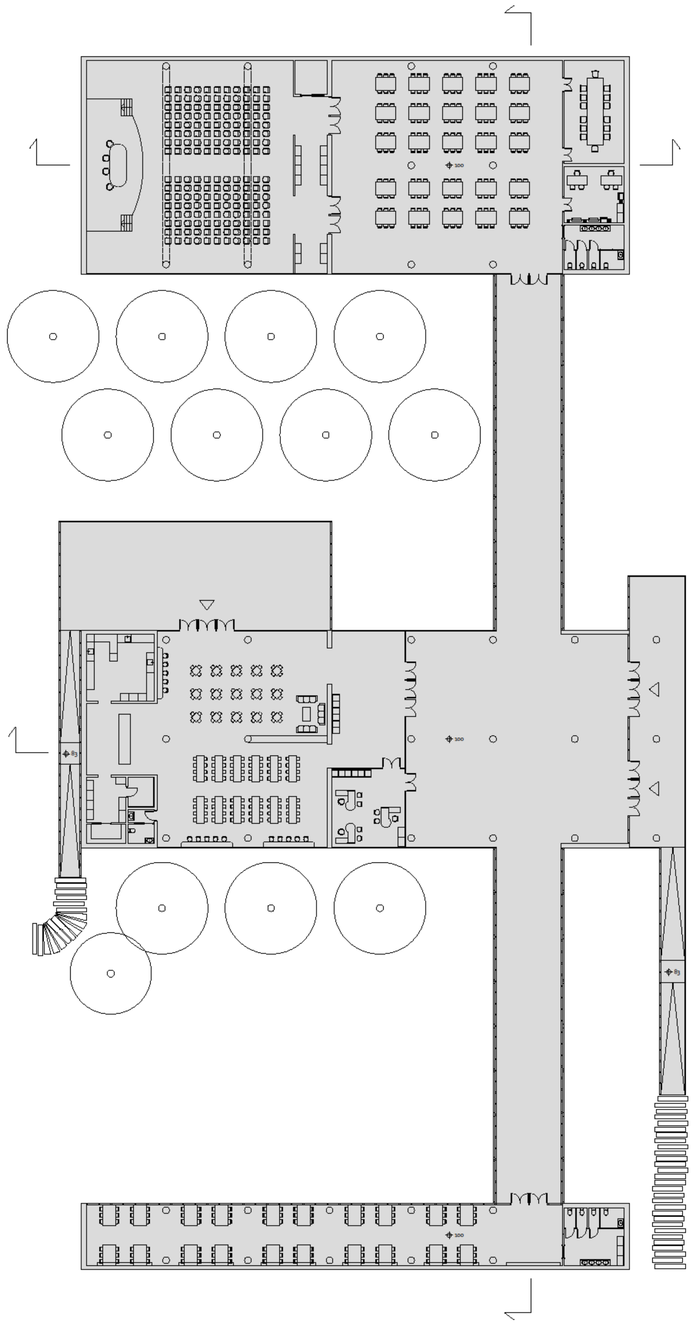

The structure is composed of three main parallel blocks, interconnected by two secondary volumetric elements that function as bridge structures and exhibition halls. The first block is the furthest downstream volume, with a width of 6 meters; while the second, central block, and the third, upper block, are characterized by a greater width, equal to 20 meters. The external perception of the blocks is deliberately opaque and monolithic, giving the building the appearance of a single, introverted block, almost "detached" from the context. In sharp contrast, the internal façades and the walls facing between the blocks feature continuous large glass windows. This formal expedient ensures maximum natural light and allows for visual perspectives between the different wings of the structure, emphasizing the exhibition hall function of the bridge structures.

Legenda della Pianta

A - Sala Conferenze
B - Disimpegno
C - Aula Studio
D - Sala Riunioni
E - Sala Stampanti
F - Servizi Igienici
G - Sala Espositiva
H - Atrio
I - Segreteria/Portineria
L - Area Bar
M - Area Ristoro
N - Cucina
O - Locale Deposito
P - Locale Tecnico

Floor Plan Legend

A - Conference Room
B - Hallway / Corridor
C - Study Room
D - Meeting Room
E - Printing Room
F - Restrooms / Toilets
G - Exhibition Room
H - Lobby / Atrium
I - Reception / Concierge
L - Bar Area
M - Refreshment Area
N - Kitchen
O - Storage Room
P - Technical Room


Pianta Piano Terra
Scala 1:200

Ground Floor Plan
Scale 1:200

DUALISMO STRUTTURALE

STRUCTURAL DUALISM

Vista Assonometrica - *Axonometric View*

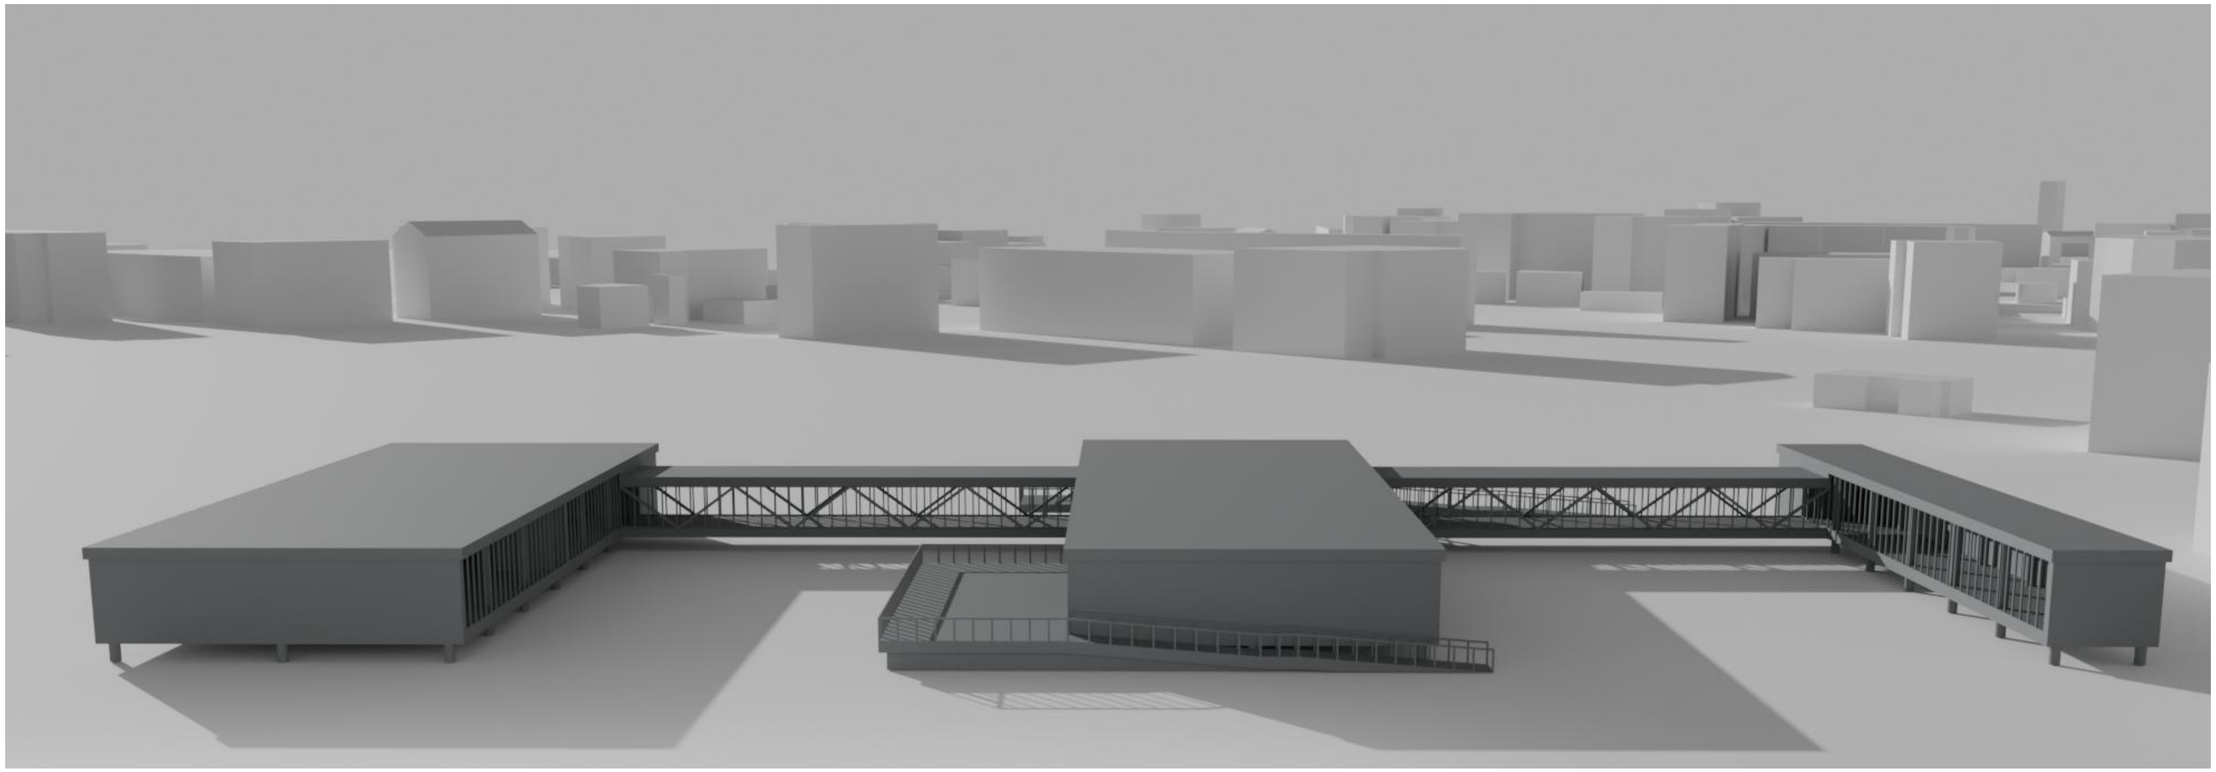


La struttura a pettine (caratterizzata da un corpo centrale e ali laterali) utilizza una differenziazione strategica delle facciate: i lati che si affacciano verso il perimetro del lotto sono mantenuti chiusi e opachi. Al contrario, le facciate che si guardano tra i tre blocchi (all'interno delle corti del pettine) sono interamente vetrate. Questo crea una potente connessione visiva e luminosa tra le diverse ali dell'edificio, massimizzando l'ingresso di luce naturale negli ambienti. In sintesi, l'edificio si presenta come una fortezza protettiva verso l'esterno, rivelando un ambiente interno trasparente, fluido e altamente illuminato.

The comb structure (characterized by a central body and side wings) utilizes a strategic differentiation of the façades: the sides facing the perimeter of the lot are kept closed and opaque. Conversely, the façades that face one another between the three blocks (inside the comb's courtyards) are entirely glazed. This creates a powerful visual and luminous connection between the different wings of the building, maximizing the entry of natural light into the spaces. In summary, the building presents itself as a protective fortress towards the exterior, revealing a transparent, fluid, and highly illuminated interior environment.

ORGANIZZAZIONE SPAZIALE
SPATIAL ORGANIZATION

Vista sull'Interno - *Interior View*

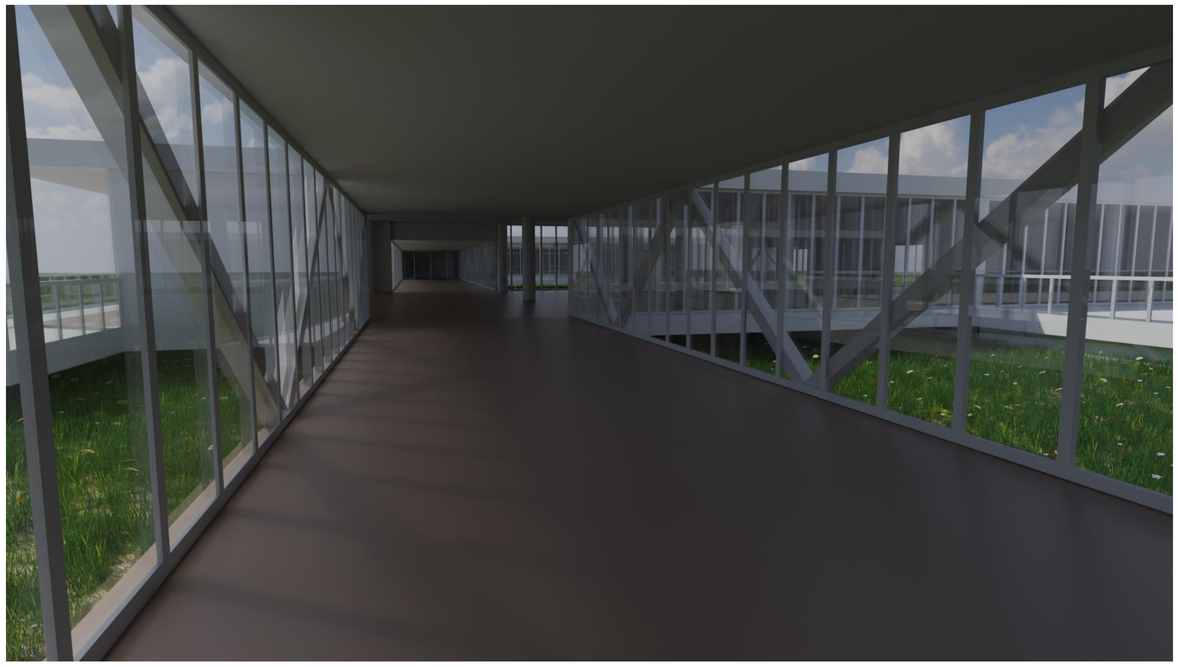

La rampa principale in basso a destra conduce all'Atrio centrale, snodo distributivo e cuore funzionale dell'edificio. Le strutture a ponte, di altezza inferiore ai blocchi principali, ospitano sale espositive con un sistema di binari per lo scorrimento di pannelli, permettendo l'allestimento di mostre temporanee.

Ogni blocco della struttura è caratterizzato da funzioni differenti. Il blocco centrale è caratterizzato da un grande atrio di fronte al quale vi è una parete vetrata dotata di due accessi che garantisce la distribuzione verso l'ufficio di gestione e accoglienza, ovvero la portineria, e verso un disimpegno che è collegato direttamente con l'area di Ristoro. L'area Ristoro e l'area Bar sono comunicanti, configurando un ampio spazio conviviale ed è presente una rampa secondaria esterna che conduce direttamente in quest'area, garantendo la possibilità di mantenere operativo questo servizio anche in orari esterni alla chiusura della struttura principale.

The main ramp at the bottom right leads to the Central Atrium, the building's distribution hub and functional core. The bridge structures, which are lower in height than the main blocks, host exhibition halls featuring a track system for sliding panels, allowing for the setup of temporary exhibitions. Each block of the structure is characterized by different functions.

The central block features a large atrium, in front of which a glazed wall with two accesses ensures distribution towards the management and reception office (i.e., the porter's lodge) and towards a hallway that is directly connected to the Refreshment area. The Refreshment area and the Bar area communicate, configuring a large convivial space, and there is a secondary external ramp that leads directly to this area, ensuring the possibility of keeping this service operational even outside the main structure's closing hours.

Vista sull'Esterno - *Exterior View*



ORGANIZZAZIONE SPAZIALE
SPATIAL ORGANIZATION

Vista sull'Interno - *Interior View*



Il blocco più a valle contiene un'ampia Aula Studio, ben illuminata e dotata di librerie integrate nella parete cieca. Infine il blocco più in alto nel lotto è dedicato a funzioni di studio e conferenze. Il blocco si articola in tre parti: nella parte centrale è presente un grande spazio per lo studio, a destra vi è una fascia di servizi: servizi igienici, un ufficio attrezzato con plotter e stampanti, e una sala riunioni; mentre a sinistra vi è un disimpegno con un locale tecnico che precede l'accesso alla Grande Sala Conferenze. La sala è caratterizzata da un'assenza di pilastri centrali grazie all'utilizzo di una struttura a travi reticolari per la copertura, ottimizzando la flessibilità dello spazio interno.

Gli spazi esterni sono valorizzati da una passerella pedonale, che connette le rampe d'accesso ai vari ingressi del lotto, e circondate da grandi alberi.

The block furthest downstream contains a large Study Hall, well-lit and equipped with integrated bookshelves in the blind wall. Finally, the block highest on the plot is dedicated to advanced study and conference functions. This block is articulated in three parts: the central part features a large study space; on the right there is a service strip: restrooms, an office equipped with plotters and printers, and a meeting room; while on the left there is a hallway with two technical rooms that precedes the access to the Grand Conference Hall. The hall is characterized by the absence of central pillars through the use of a truss structure for the roof, optimizing the flexibility of the internal space.
The outdoor spaces are enhanced by a pedestrian walkway, which connects the access ramps to the various entrances of the plot, and are surrounded by large trees.


Vista sull'Esterno - *Exterior View*



ELABORATI GRAFICI DI PROGETTO

PROJECT DRAWINGS

Prospetto Nord-Est – *North-East Elevation*
Scala 1:100 – *Scale 1:100*

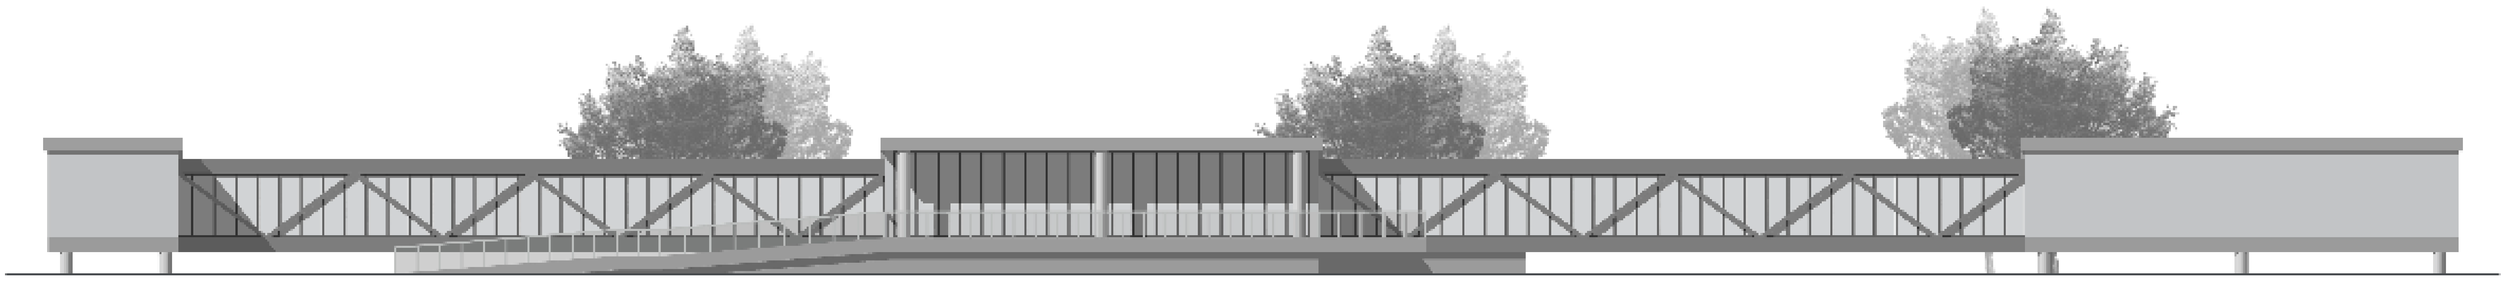

Prospetto Sud-Ovest – *South-West Elevation*
Scala 1:100 – *Scale 1:100*




ELABORATI GRAFICI DI PROGETTO

PROJECT DRAWINGS

Sezione 1-1 – *Section 1-1*
Scala 1:100 – *Scale 1:100*




Sezione 2-2 – *Section 2-2*
Scala 1:100 – *Scale 1:100*

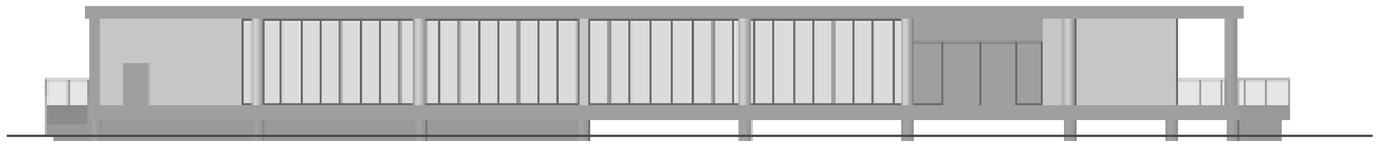


Sezione 3-3 – *Section 3-3*
Scala 1:100 – *Scale 1:100*



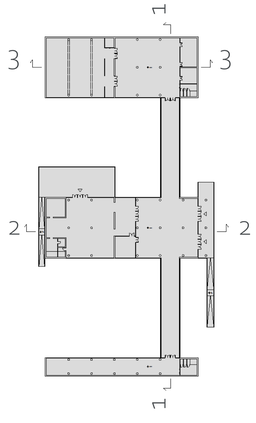

DETTAGLI STRUTTURALI

STRUCTURAL DETAILS

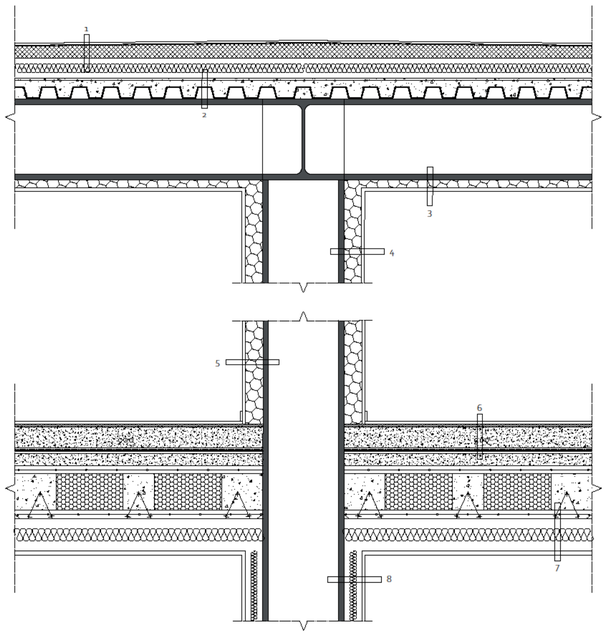

Scala 1:10 – *Scale 1:10*

Legenda Dettagli Strutturali

1. Pavimentazione, guaina bituminosa sp.4mm, massetto di pendenza, al di sotto isolante sp. 10cm;
2. Pacchetto strutturale in lamiera grecata con getto e rete elettrosaldata;
3. Pannello ignifugo sp. 4cm e pannello in cartongesso sp. 8cm;
4. Intonaco sp. 1.5cm, isolamento a cappotto sp. 10cm, pilastro in acciaio.
5. Intonaco sp. 1.5cm, riempimento a nido d'ape sp. 10cm, pilastro in acciaio
6. Pavimentazione sp. 1cm, getto autolivellante sp. 1cm, massetto portaimpianti in cls alleggerito sp. 10cm, isolante sp. 3cm.
7. Solaio a lastra predalles 4+18+4, isolamento a cappotto cp. 16cm e intornaco sp. 1.5cm.
8- 9. Intonaco sp. 1.5cm, isolamento a cappotto sp. 10cm, pilastro in acciaio.
10. Ferri di ancoraggio e armature del plinto;
11. Magrone sp. 10cm, fondazione a plinto, guaina impermeabilizzante sp. 3mm e coprimembrana sp. 3mm.

Legend of Structural Details

1. Flooring, bituminous membrane (4mm), sloping screed and insulation (10cm).
2. Structural deck package in corrugated sheet metal with cast concrete and electrowelded mesh.
3. Fireproof panel (4cm) and plasterboard panel (8cm).
4. Plaster (thickness 1.5cm), external thermal insulation composite system (10cm), steel column/pillar.
5. Plaster (1.5cm), honeycomb infill (10cm), reinforced concrete column/pillar.
6. Flooring (1cm), self-leveling screed (1cm), lightweight concrete service screed (10cm), insulation (3cm).
7. Predalles slab (4+18+4), external cladding insulation (16cm), and plaster (1.5cm).
8 - 9. Plaster (1.5cm), external cladding insulation (10cm), steel column/pillar.
10. Anchoring bars and footing reinforcement / rebar.
11. Lean concrete/blinding layer (10cm), pad foundation/isolated footing, waterproofing membrane (3mm) and membrane cover (3mm).

GRAZIE PER L'ATTENZIONE!

