
OLTRE LE MURA: LE TRE DIMENSIONI DELL'ABITARE

MENTE - CORPO - CASA

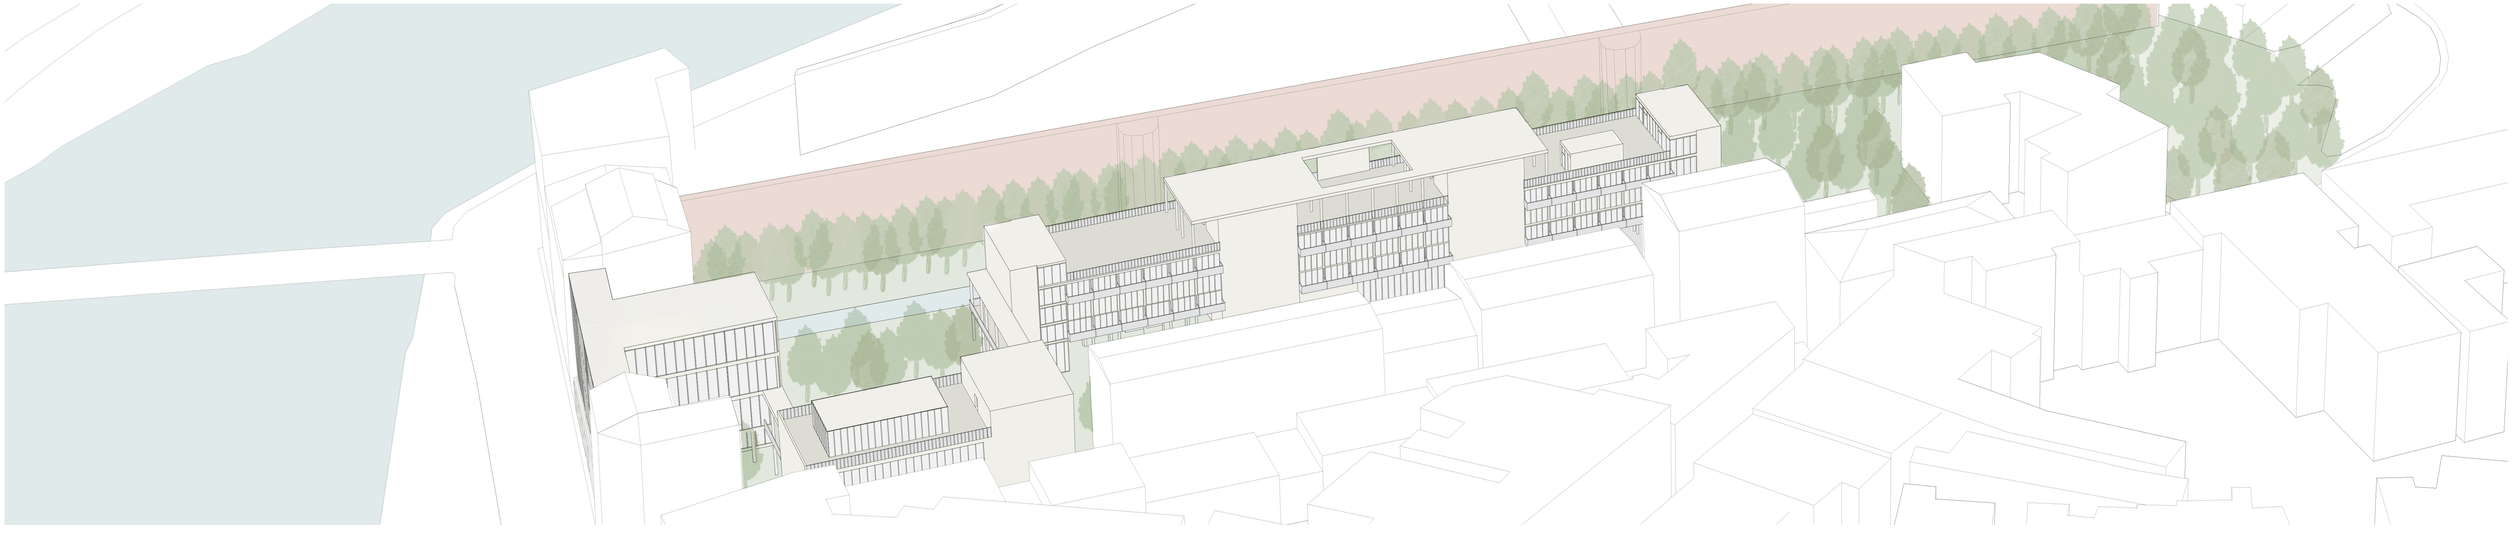

UNIVERSITÀ DI PISA

CDLM in INGEGNERIA EDILE-ARCHITETTURA
DEGREE IN BUILDING ENGINEERING-ARCHITECTURE

LAB. INTEGRATO DI PROGETTAZIONE ARCHITETTONICA III
INTEGRATED ARCHITECTURAL DESIGN STUDIO III

INSEGNAMENTO - COMPOSIZIONE ARCHITETTONICA
COURSE - ARCHITECTURAL COMPOSITION

DOCENTI - Prof. Arch. Luca Lanini, Prof. Ing. Antonio Mariano
TUTOR - Prof. Arch. Luca Lanini, Prof. Ing. Antonio Mariano

ALLIEVE/*STUDENTS* - Alice Betti, Giada Liberto, Matilde Orsini

OLTRE LE MURA: LE TRE DIMENSIONI DELL'ABITARE

CONCEPT

Il progetto propone una rigenerazione urbana del delicato e storico tessuto pisano, inserendosi strategicamente nell'area compresa tra il Lungarno Galileo Galilei, Via Giovanni Bovio e i margini del Giardino Scotto. Il masterplan si articola in tre poli funzionali distinti ma sinergici, concepiti per rispondere alle esigenze della comunità universitaria e cittadina secondo tre sfere fondamentali dell'individuo: la "Mente" (Polo Polifunzionale), il "Corpo" (Polo Sportivo) e la "Casa" (Polo Residenziale). L'obiettivo urbanistico è ricucire il fronte fluviale con il parco retrostante, generando una nuova permeabilità attraverso piazze pubbliche, percorsi alberati e volumi puri che ridefiniscono lo spazio senza occluderlo.

The project proposes an urban regeneration of the delicate and historic Pisan fabric, strategically inserting itself in the area between Lungarno Galileo Galilei, Via Giovanni Bovio, and the edges of the Giardino Scotto. The masterplan is divided into three distinct but synergistic functional hubs, conceived to meet the needs of the university and city community according to three fundamental spheres of the individual: the "Mind" (Multi-purpose Center) , the "Body" (Sports Center) , and the "Home" (Residential Hub). The urban objective is to stitch the riverfront back together with the park behind it, generating new permeability through public squares, tree-lined paths, and pure volumes that redefine the space without occluding it.

RIFERIMENTI PROGETTUALI - *PROJECT REFERENCES*

Il linguaggio compositivo trae una forte ispirazione dai maestri del Movimento Moderno, con un chiaro rimando al razionalismo di Le Corbusier. I principi dei 'Cinque Punti dell'Architettura' sono leggibili nell'uso dei pilotis che sollevano i volumi da terra, garantendo la continuità visiva e fisica dei percorsi pedonali al piano terra, e nella presenza di coperture piane e facciate libere. L'ampio utilizzo di superfici vetrate, alternate a una struttura in calcestruzzo a vista ed elementi strutturali snelli, si contrappone dialetticamente alla matericità delle preesistenze storiche, instaurando un dialogo tra contemporaneità e memoria del luogo che riecheggia la purezza formale di Mies van der Rohe.

The compositional language draws strong inspiration from the masters of the Modern Movement, with a clear nod to Le Corbusier's Rationalism. The principles of his 'Five Points of Architecture' are evident in the use of pilotis that lift the volumes off the ground—ensuring the physical and visual continuity of the pedestrian pathways on the ground floor—as well as in the presence of flat roofs and free facades. The extensive use of glazed surfaces, alternating with an exposed concrete structure and slender structural elements, stands in dialectical contrast to the materiality of the historic pre-existences, establishing a dialogue between modernity and the memory of the place that echoes the formal purity of Mies van der Rohe

Legenda - *Key*

A. Polo Polifunzionale con Aule, Laboratori e Spazi Espositivi - *Multipurpose Centre with Classrooms, Laboratories and Exhibition Spaces.*

B. Polo Sportivo con Piscina, Palestra e Campo da Padel - *Sports Centre with Swimming Pool, Gym and Padel Court.*

C. Polo Residenziale con Mensa Universitaria, Lavanderie e Spazi Ricreativi - *Residential Hub with University Canteen, Laundries and Social Spaces.*

D: Specchio d'acqua - Water feature

E: Servizi specialistici del parco (dotazioni sportive, aree per il relax, socialità e studio) - *Specialized park services (sports facilities, areas for relaxation, socializing and study)*

Area di Progetto - *Project Area*

Foto Inserimento di Progetto - *Project Photomontage*



Planimetria - *Site Plan*
Scala 1:500 - *Scale 1:500*



UNIVERSITÀ DI PISA

CDLM in INGEGNERIA EDILE-ARCHITETTURA
DEGREE IN BUILDING ENGINEERING-ARCHITECTURE

LAB. INTEGRATO DI PROGETTAZIONE ARCHITETTONICA III
INTEGRATED ARCHITECTURAL DESIGN STUDIO III

INSEGNAMENTO - COMPOSIZIONE ARCHITETTONICA
COURSE - ARCHITECTURAL COMPOSITION

DOCENTI - Prof. Arch. Luca Lanini, Prof. Ing. Antonio Mariano
TUTOR - Prof. Arch. Luca Lanini, Prof. Ing. Antonio Mariano

ALLIEVE/*STUDENTS* - Alice Betti, Giada Liberto, Matilde Orsini


MENTE - *MIND*

CONCEPT


Affacciato sul Lungarno Galileo Galilei, questo edificio è il fulcro culturale e intellettuale dell'intero intervento. Sul fronte principale verso il fiume, il restauro dei resti storici dialoga con un moderno volume retrostante di quattro piani: una struttura interamente vetrata che accoglie un ampio spazio espositivo e prevede una scalinata scenografica che unisce i vari livelli. Da questo corpo trasparente si sviluppa un'ala dedicata a laboratori, aule didattiche e sale conferenze. L'architettura gioca sulla massima accessibilità: il piano terra accoglie i flussi pedonali guidandoli verso il parco interno, mentre il primo piano si collega fluidamente agli altri edifici del complesso grazie a un percorso aereo sopraelevato.

Overlooking the Lungarno Galileo Galilei, this building is the cultural and intellectual hub of the entire project. On the main front facing the river, the restoration of the historic remains dialogues with a modern four-story volume behind it: an entirely glass structure that houses a large exhibition space and features a scenic staircase that connects the various levels. From this transparent body develops a wing dedicated to laboratories, classrooms and conference rooms. The architecture plays on maximum accessibility: the ground floor accommodates pedestrian flows by guiding them towards the internal park, while the first floor connects fluidly to the other buildings in the complex thanks to an elevated aerial path.


Pianta Piano Terra - *Ground Floor Plan*
Scala 1:200 - *Scale 1:200*

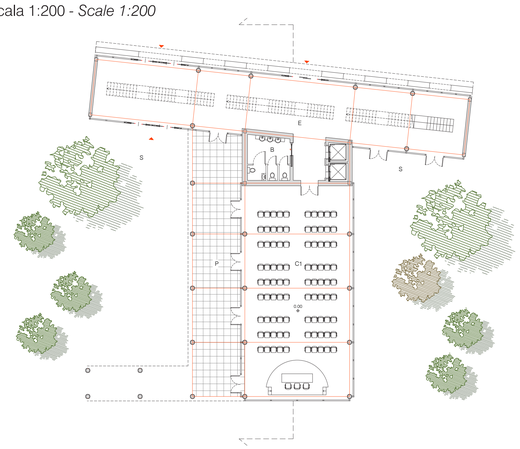


Pianta Piano Primo - *First Floor Plan*
Scala 1:200 - *Scale 1:200*

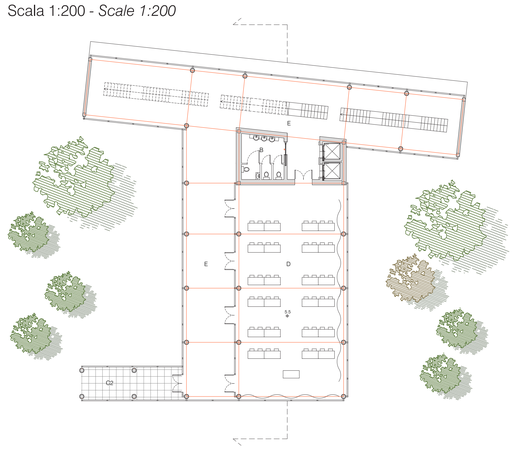

Pianta Piano Secondo - *Second Floor Plan*
Scala 1:200 - *Scale 1:200*

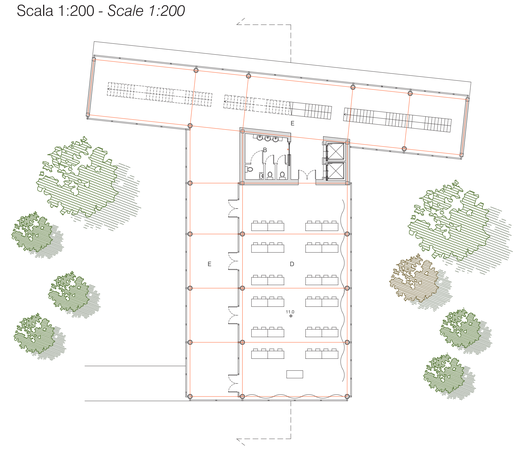

Dettaglio Strutturale - *Structural Details*
Scala 1:50 - *Scale 1:50*

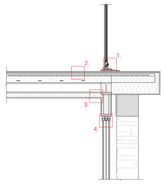


1. Infisso in alluminio, con vetro camera sp. 4+16+4, soglia in alluminio - *Aluminum window frame, with 4+16+4 mm double glazing, aluminum threshold.*

2. Pavimentazione 2 cm, materassino anticalpestio sp. 1 cm, isolante sp. 3 cm soletta collaborante con rete elettrosaldata sp. 5 cm, massetto portaimpianti sp. 15 cm - *2 cm flooring, 1 cm thk. acoustic underlay (impact sound insulation), 3 cm thk. insulation, 5 cm thk. composite slab with welded wire mesh, 15 cm thk. service screed*


3. Trave HEB h.24 cm isolante sp. 10 cm, rasatura sp. 2 cm - *HEB beam h. 24 cm, 10 cm thk. insulation, 2 cm thk. skim coat*

4. Architrave, isolante, telaio in alluminio, porta scorrevole in vetro - *Lintel, insulation, aluminum frame, sliding glass door*

Pianta Piano Terzo - *Third Floor Plan*
Scala 1:200 - *Scale 1:200*

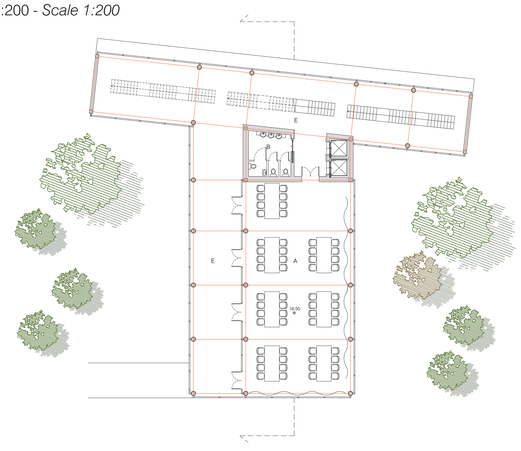


Pianta Piano Copertura - *Roof Plan*
Scala 1:200 - *Scale 1:200*

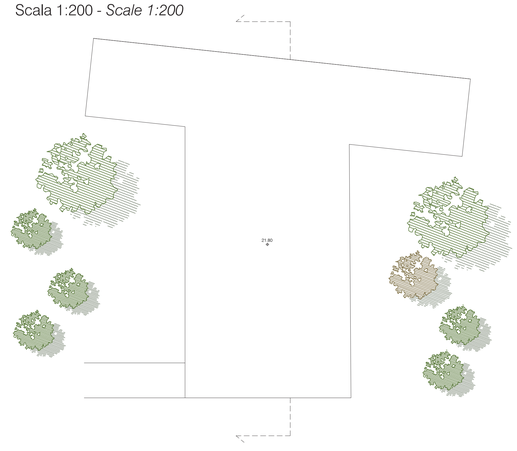


Rendering Lungarno - *Lungarno View*



Sezione - *Section*
Scala 1:200 - *Scale 1:200*

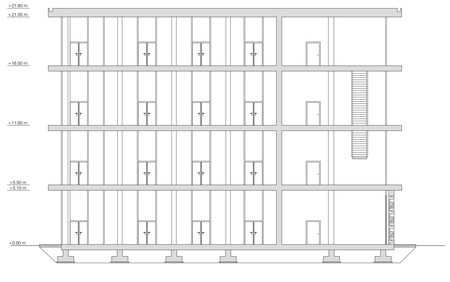

Prospetto Lungarno - *Lungarno Front*
Scala 1:200 - *Scale 1:200*

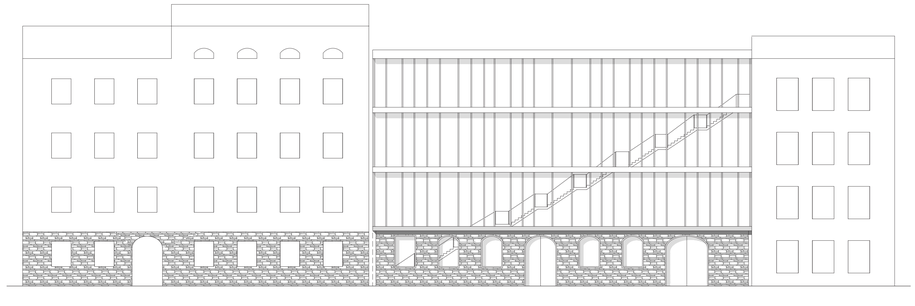

UNIVERSITÀ DI PISA

CDLM in INGEGNERIA EDILE-ARCHITETTURA
DEGREE IN BUILDING ENGINEERING-ARCHITECTURE

LAB. INTEGRATO DI PROGETTAZIONE ARCHITETTONICA III
INTEGRATED ARCHITECTURAL DESIGN STUDIO III

INSEGNAMENTO - COMPOSIZIONE ARCHITETTONICA
COURSE - ARCHITECTURAL COMPOSITION

DOCENTI - Prof. Arch. Luca Lanini, Prof. Ing. Antonio Mariano
TUTOR - Prof. Arch. Luca Lanini, Prof. Ing. Antonio Mariano

ALLIEVE/*STUDENTS* - Alice Betti, Giada Liberto, Matilde Orsini

CORPO - *BODY*

CONCEPT


Il Polo Sportivo, scandito da linee pulite ed essenziali, si configura come il cuore pulsante del benessere e del movimento. Il complesso accoglie una piscina al piano terra, una palestra attrezzata al primo piano e un campo da padel sulla terrazza all'ultimo piano, uniformandosi all'altezza degli edifici vicini. L'architettura celebra la massima trasparenza: le grandi facciate vetrate svelano le attività interne e, all'imbrunire, trasformano l'edificio in una suggestiva "lanterna" dinamica. Questo dialogo visivo costante con il verde circostante valorizza il paesaggio e offre alla comunità un nuovo spazio di socialità giovanile.

The Sports Center, marked by clean and essential lines, is configured as the beating heart of well-being and movement. The complex features a swimming pool on the ground floor, a fully equipped gym on the first floor, and a padel court on the terrace on the top floor, matching the height of the nearby buildings. The architecture celebrates maximum transparency: the large glass facades reveal the internal activities and, at dusk, transform the building into an evocative dynamic "lantern". This constant visual dialogue with the surrounding greenery enhances the landscape and offers the community a new space for youthful sociality.


Rendering Polo Sportivo, Via Bovio - *Sports Centre Rendering, Bovio Street*




Pianta Piano Terra - *Ground Floor Plan*
Scala 1:200 - *Scale 1:200*

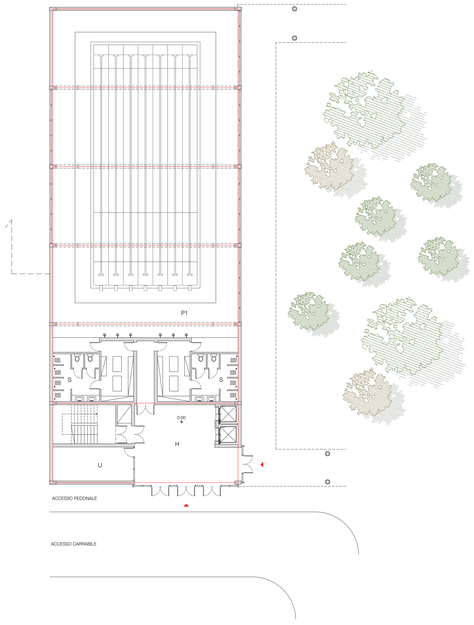


Pianta Piano Primo - *First Floor Plan*
Scala 1:200 - *Scale 1:200*

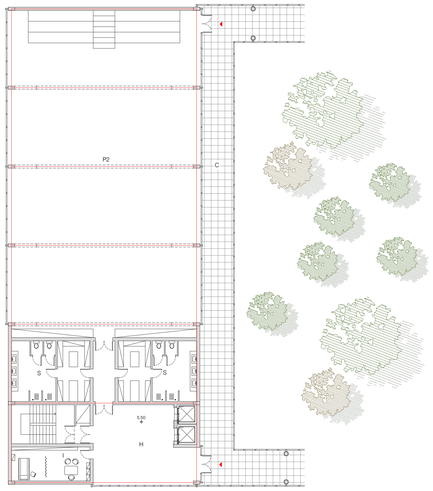

Pianta Piano Secondo - *Second Floor Plan*
Scala 1:200 - *Scale 1:200*

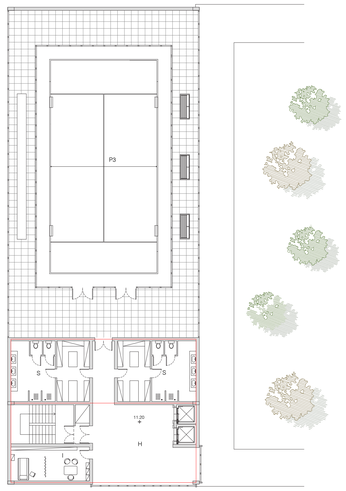

Pianta Piano Copertura - *Roof Plan*
Scala 1:200 - *Scale 1:200*

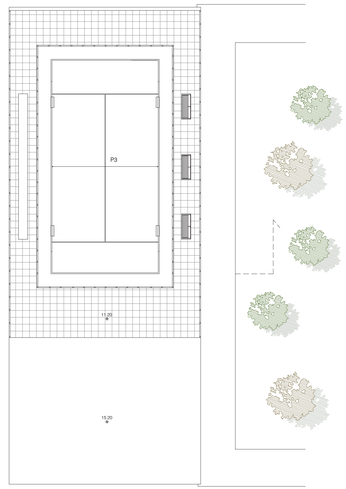


LEGENDA/KEY
C - Corridoio Esterno/*Outer Corridor*
H - Ingresso/ *Hall*
I - Infermeria/ *Nurse*
P1 - Piscina/ *Swimming Pool*
P2 - Palestra/ *Gym*
P3 - Campo da Padel/ *Padel Court*
U - Uffici Amministrativi/ *Administration Offices*


Rendering Polo Sportivo - *Sports Centre Rendering*




Sezione - *Section*
Scala 1:200 - *Scale 1:200*

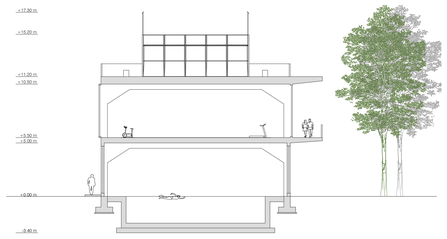

Prospetto Nord-Est - *North-East Front*
Scala 1:200 - *Scale 1:200*

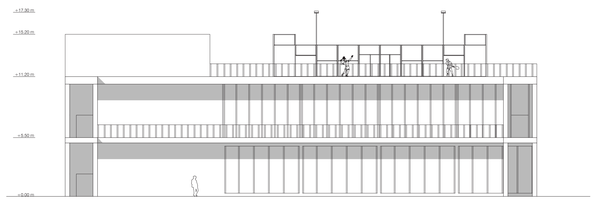

Prospetto via Giovanni Bovio - *Giovanni Bovio Street View*
Scala 1:200 - *Scale 1:200*

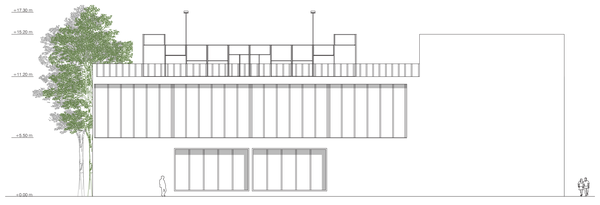

UNIVERSITÀ DI PISA

CDLM in INGEGNERIA EDILE-ARCHITETTURA
DEGREE IN BUILDING ENGINEERING-ARCHITECTURE

LAB. INTEGRATO DI PROGETTAZIONE ARCHITETTONICA III
INTEGRATED ARCHITECTURAL DESIGN STUDIO III


INSEGNAMENTO - COMPOSIZIONE ARCHITETTONICA
COURSE - ARCHITECTURAL COMPOSITION

DOCENTI - Prof. Arch. Luca Lanini, Prof. Ing. Antonio Mariano
TUTOR - Prof. Arch. Luca Lanini, Prof. Ing. Antonio Mariano

ALLIEVE/*STUDENTS* - Alice Betti, Giada Liberto, Matilde Orsini

CASA - *HOME*


Pianta Piano Terra - *Ground Floor Plan*
Scala 1:200 - *Scale 1:200*

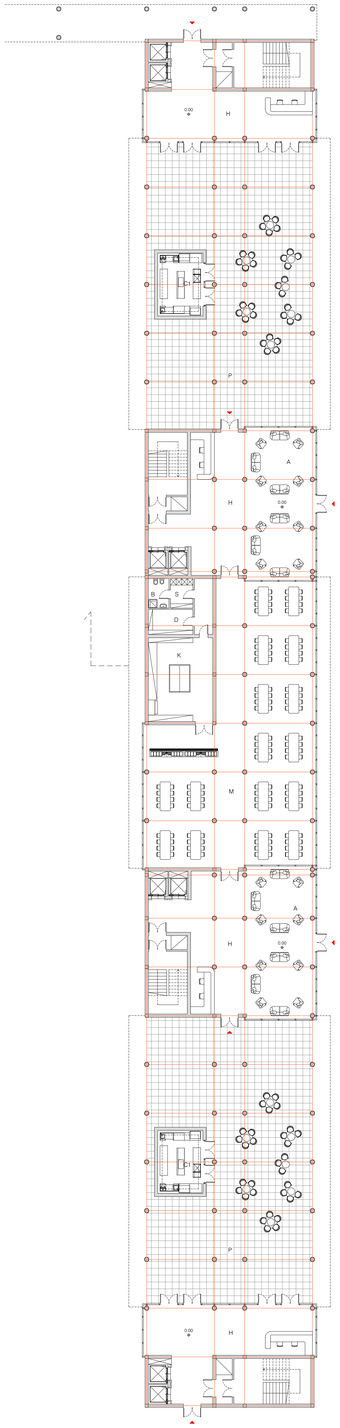


Pianta Piano Primo - *First Floor Plan*
Scala 1:200 - *Scale 1:200*




Pianta Piano Secondo - *Second Floor Plan*
Scala 1:200 - *Scale 1:200*

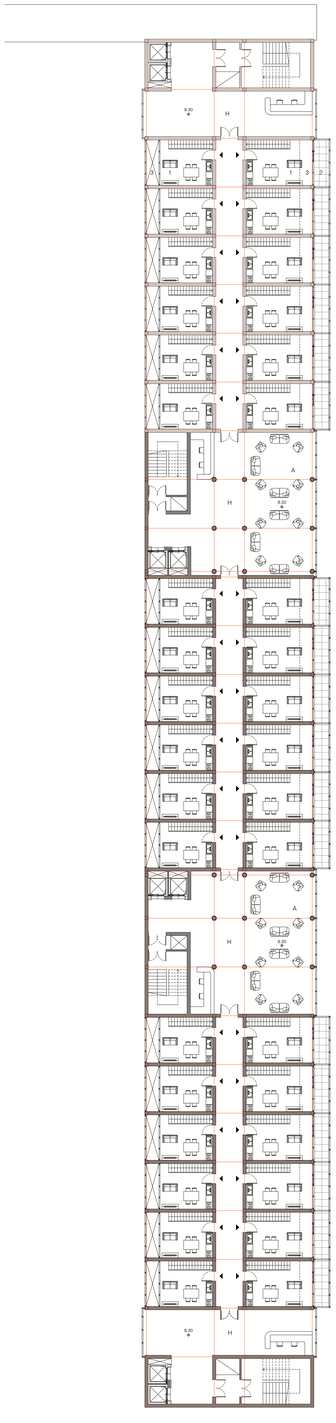


Pianta Piano Terzo - *Third Floor Plan*
Scala 1:200 - *Scale 1:200*

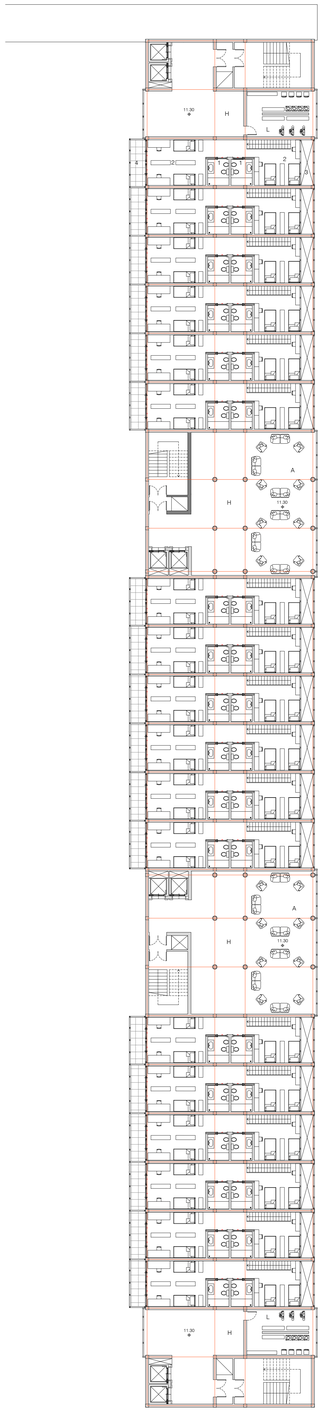

Pianta Piano Quarto - *Fourth Floor Plan*
Scala 1:200 - *Scale 1:200*

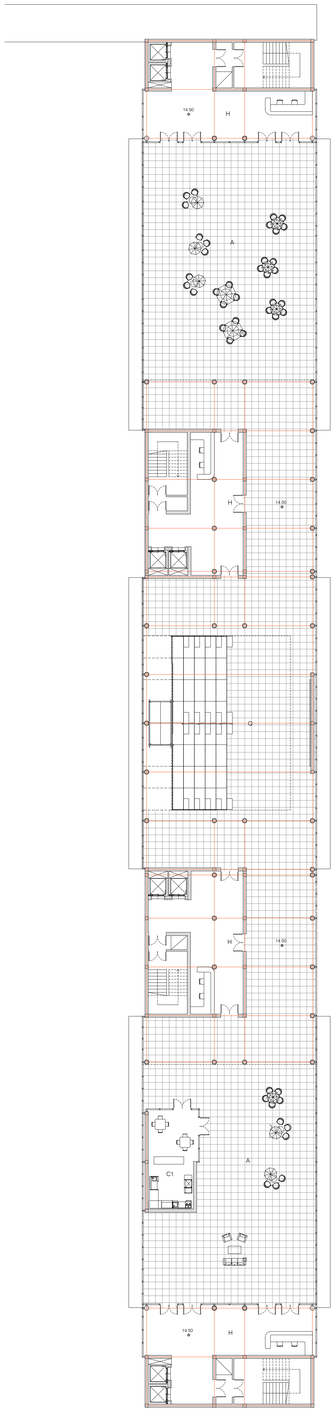

Pianta Piano Copertura - *Roof Plan*
Scala 1:200 - *Scale 1:200*

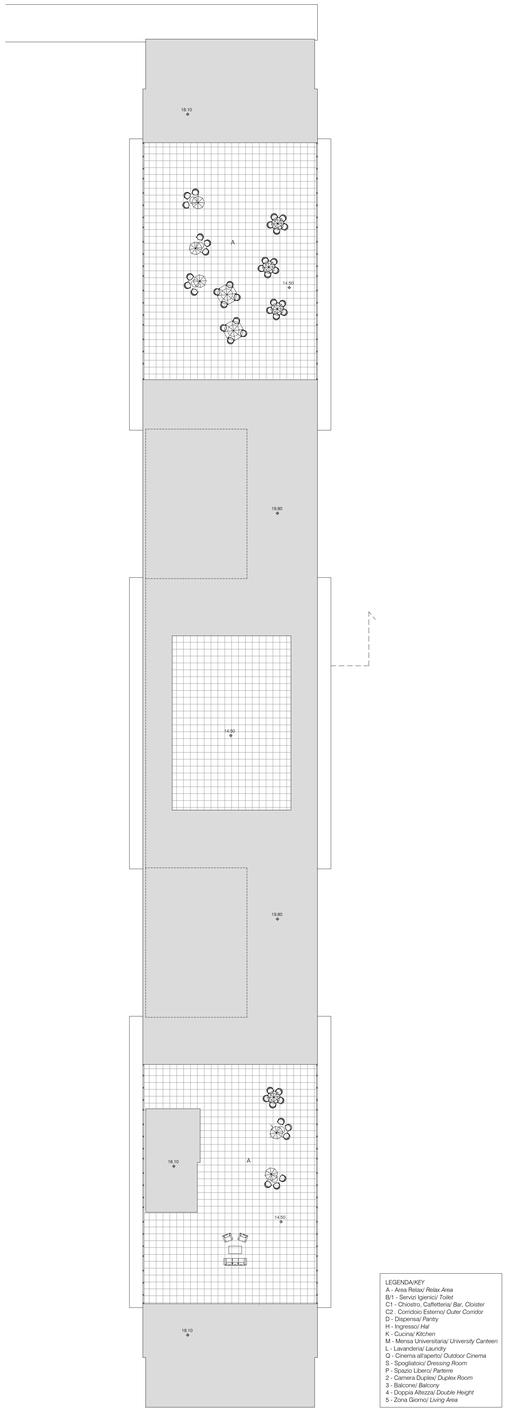

UNIVERSITÀ DI PISA

CDLM in INGEGNERIA EDILE-ARCHITETTURA
DEGREE IN BUILDING ENGINEERING-ARCHITECTURE

LAB. INTEGRATO DI PROGETTAZIONE ARCHITETTONICA III
INTEGRATED ARCHITECTURAL DESIGN STUDIO III

INSEGNAMENTO - COMPOSIZIONE ARCHITETTONICA
COURSE - ARCHITECTURAL COMPOSITION

DOCENTI - Prof. Arch. Luca Lanini, Prof. Ing. Antonio Mariano
TUTOR - Prof. Arch. Luca Lanini, Prof. Ing. Antonio Mariano

ALLIEVE/*STUDENTS* - Alice Betti, Giada Liberto, Matilde Orsini


CASA - *HOME*

CONCEPT


Il Polo Residenziale si sviluppa longitudinalmente attraverso una stecca rigorosa, configurandosi come un filtro architettonico tra i palazzi della città universitaria e il verde storico del Giardino Scotto. L'edificio non è concepito come semplice dormitorio, ma come un vero e proprio hub di vita, che integra le unità abitative con servizi essenziali alla collettività studentesca e spazi pubblici che favoriscono la socializzazione, come mensa universitaria e chioschi al piano terra e cinema all'aperto sulla terrazza dell'ultimo piano. Il progetto rilegge il tema dell'edilizia residenziale di Le Corbusier de l'Unite d'Habitation, grazie alle sue cellule abitative sviluppate su 3 piani, i prospetti scanditi da logge e il tetto giardino con spazi pubblici, ma lo aggiorna adattandolo alle esigenze di interazione e condivisione della vita studentesca contemporanea.

The Residential Center develops longitudinally through a rigorous strip, configuring itself as an architectural filter between the buildings of the university city and the historic greenery of the Scotto Garden. The building is not conceived as a simple dormitory, but as a true hub of life, integrating residential units with essential services for the student community and public spaces that foster socialization, such as a university cafeteria and kiosks on the ground floor and an open-air cinema on the top-floor terrace. The project reinterprets the theme of residential construction by Le Corbusier de l'Unite d'Habitation, thanks to its three-story residential cells, elevations punctuated by loggias, and a garden roof with public spaces, but updates it to adapt it to the needs of contemporary student life for interaction and sharing.


Cellula Abitativa: Piano Primo - *Housing Cell: First Floor*
Scala 1:100 - *Scale 1:100*

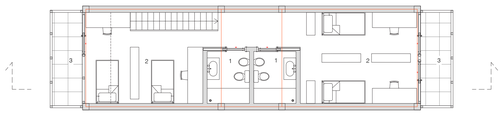

Cellula Abitativa: Piano Primo - *Housing Cell: First Floor*
Scala 1:100 - *Scale 1:100*

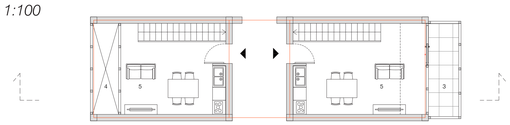

Cellula Abitativa: Piano Primo - *Housing Cell: First Floor*
Scala 1:100 - *Scale 1:100*

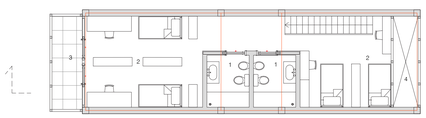

Legenda - *Key*	3. Balcone - *Balcony*
1. Servizi Igienici - *Toilet*	4. Doppia Altezza - *Double Height*
2. Camera Duplex - *Duplex Room*	5. Zona Giorno - *Living Area*


Cellula Abitativa: Sezione - *Housing Cell: Section*
Scala 1:100 - *Scale 1:100*



Prospetto Sud-Est - *South-East Elevation*
Scala 1:200 - *Scale 1:200*



Prospetto Nord-Ovest - *North-West Elevation*
Scala 1:200 - *Scale 1:200*

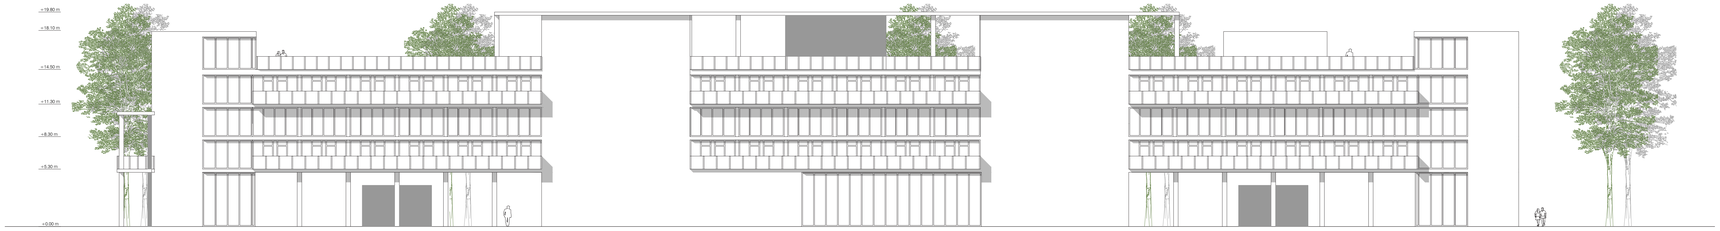

Rendering Parco - *Green Area Rendering*



Rendering Polo Residenziale - *Residential Complex Rendering*



UNIVERSITÀ DI PISA

CDLM in INGEGNERIA EDILE-ARCHITETTURA
DEGREE IN BUILDING ENGINEERING-ARCHITECTURE

LAB. INTEGRATO DI PROGETTAZIONE ARCHITETTONICA III
INTEGRATED ARCHITECTURAL DESIGN STUDIO III

INSEGNAMENTO - COMPOSIZIONE ARCHITETTONICA
COURSE - ARCHITECTURAL COMPOSITION

DOCENTI - Prof. Arch. Luca Lanini, Prof. Ing. Antonio Mariano
TUTOR - Prof. Arch. Luca Lanini, Prof. Ing. Antonio Mariano

ALLIEVE/*STUDENTS* - Alice Betti, Giada Liberto, Matilde Orsini